

# LOT 4, 5 & 6 WOOD HAVEN

618 CAVAN ROAD. DALLAS, TX 75223

Sheet Number	Sheet Name	Sheet Discipline
A100	COVER SHEET	
A101	SITE PLAN	
A102	WAREHOUSE FLOOR PLAN	
A102A	WAREHOUSE ROOF PLAN	
A103	WAREHOUSE ELEVATIONS	
A104	HOUSE GROUND FLOOR PLAN	
A104A	HOUSE ROOF LEVEL PLAN	
A107	BUILDING ELEVATIONS	

CONTRACTOR  
KASSABILT LLC



ISSUES

NO.	DATE	DESCRIPTION

## LOT 6, BLOCK 31/1615 MOUNT AUBURN

500/502 S GLASGOW DR. DALLAS, TX 75223

PARCEL ID: 00000166051000000

DALLAS COUNTY, TEXAS



Copyright (C) 2023 by KEILEY & KASSA COMMUNITIES LLC.  
All drawings, specifications and other documents prepared by the designer  
are the sole and exclusive property of Keiley & Kassa Communities LLC and are  
solely with respect to this project and unless otherwise provided, Kassabilt  
LLC shall have no rights, title or interest in them. They are to be held in confidence  
common law, statutory and other reserved rights, including the copyrights.  
Copies of architectural drawings, specifications and other documents  
for information or reference are prohibited unless expressly authorized by  
Kassabilt LLC in writing.

OWNER  
KEILEY & KASSA COMMUNITIES LLC - SERIES 1  
500/502 S GLASGOW DR.DALLAS, TX 75223


JOB NO.  
DATE 08/01/2024  
DRAWN BY Author  
CHECKED BY Checker  
PHASE  
SHEET NAME  
COVER SHEET

SHEET NUMBER  
**A100**

OWNER	GENERAL CONTRACTOR	ARCHITECT	MEP & STRUCTURES	
KEILEY & KASSA COMMUNITIES LLC - SERIES 1	KASSABILT LLC	Ar.FAAIZA ZAFAR	MINA MIKAEEL KIRO ENGINEERING	

# **TRACTOR BILT LLC**

ABILITY LLC

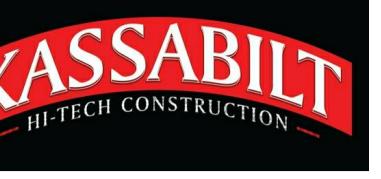

ES

**Lot 6, BLOCK 31/1615 MOUNT AUBURN**

500/502 S GLASGOW DR. DALLAS, TX 75223

PARCEL ID: 0000016605100000


DALLAS COUNTY, TEXAS

(C) 2023 by KEILEY & KASSA COMMUNITIES LLC.  
Logs, specifications and other documents prepared by the designer  
consultants for this project are instruments of Kabasilit LLC for use  
with respect to this project and unless otherwise provided, Kabasilit  
shall be deemed the author of these documents and shall retain all  
law, statutory and other reserved rights, including the copyrights,  
architectural drawings, specifications and other documents for  
which reference are prohibited unless expressly authorized by  
LLC in writing

NER  
Y & KASSA COMMUNITIES LLC - SERIES 1  
02 S GLASGOW DR.DALLAS, TX 75223

<b>NO.</b>	
<b>E</b>	08/01/2024
<b>WN BY</b>	F.Z
<b>CKED BY</b>	J.K
<b>SE</b>	
<b>T NAME</b>	PLAN

# ART NUMBER 101

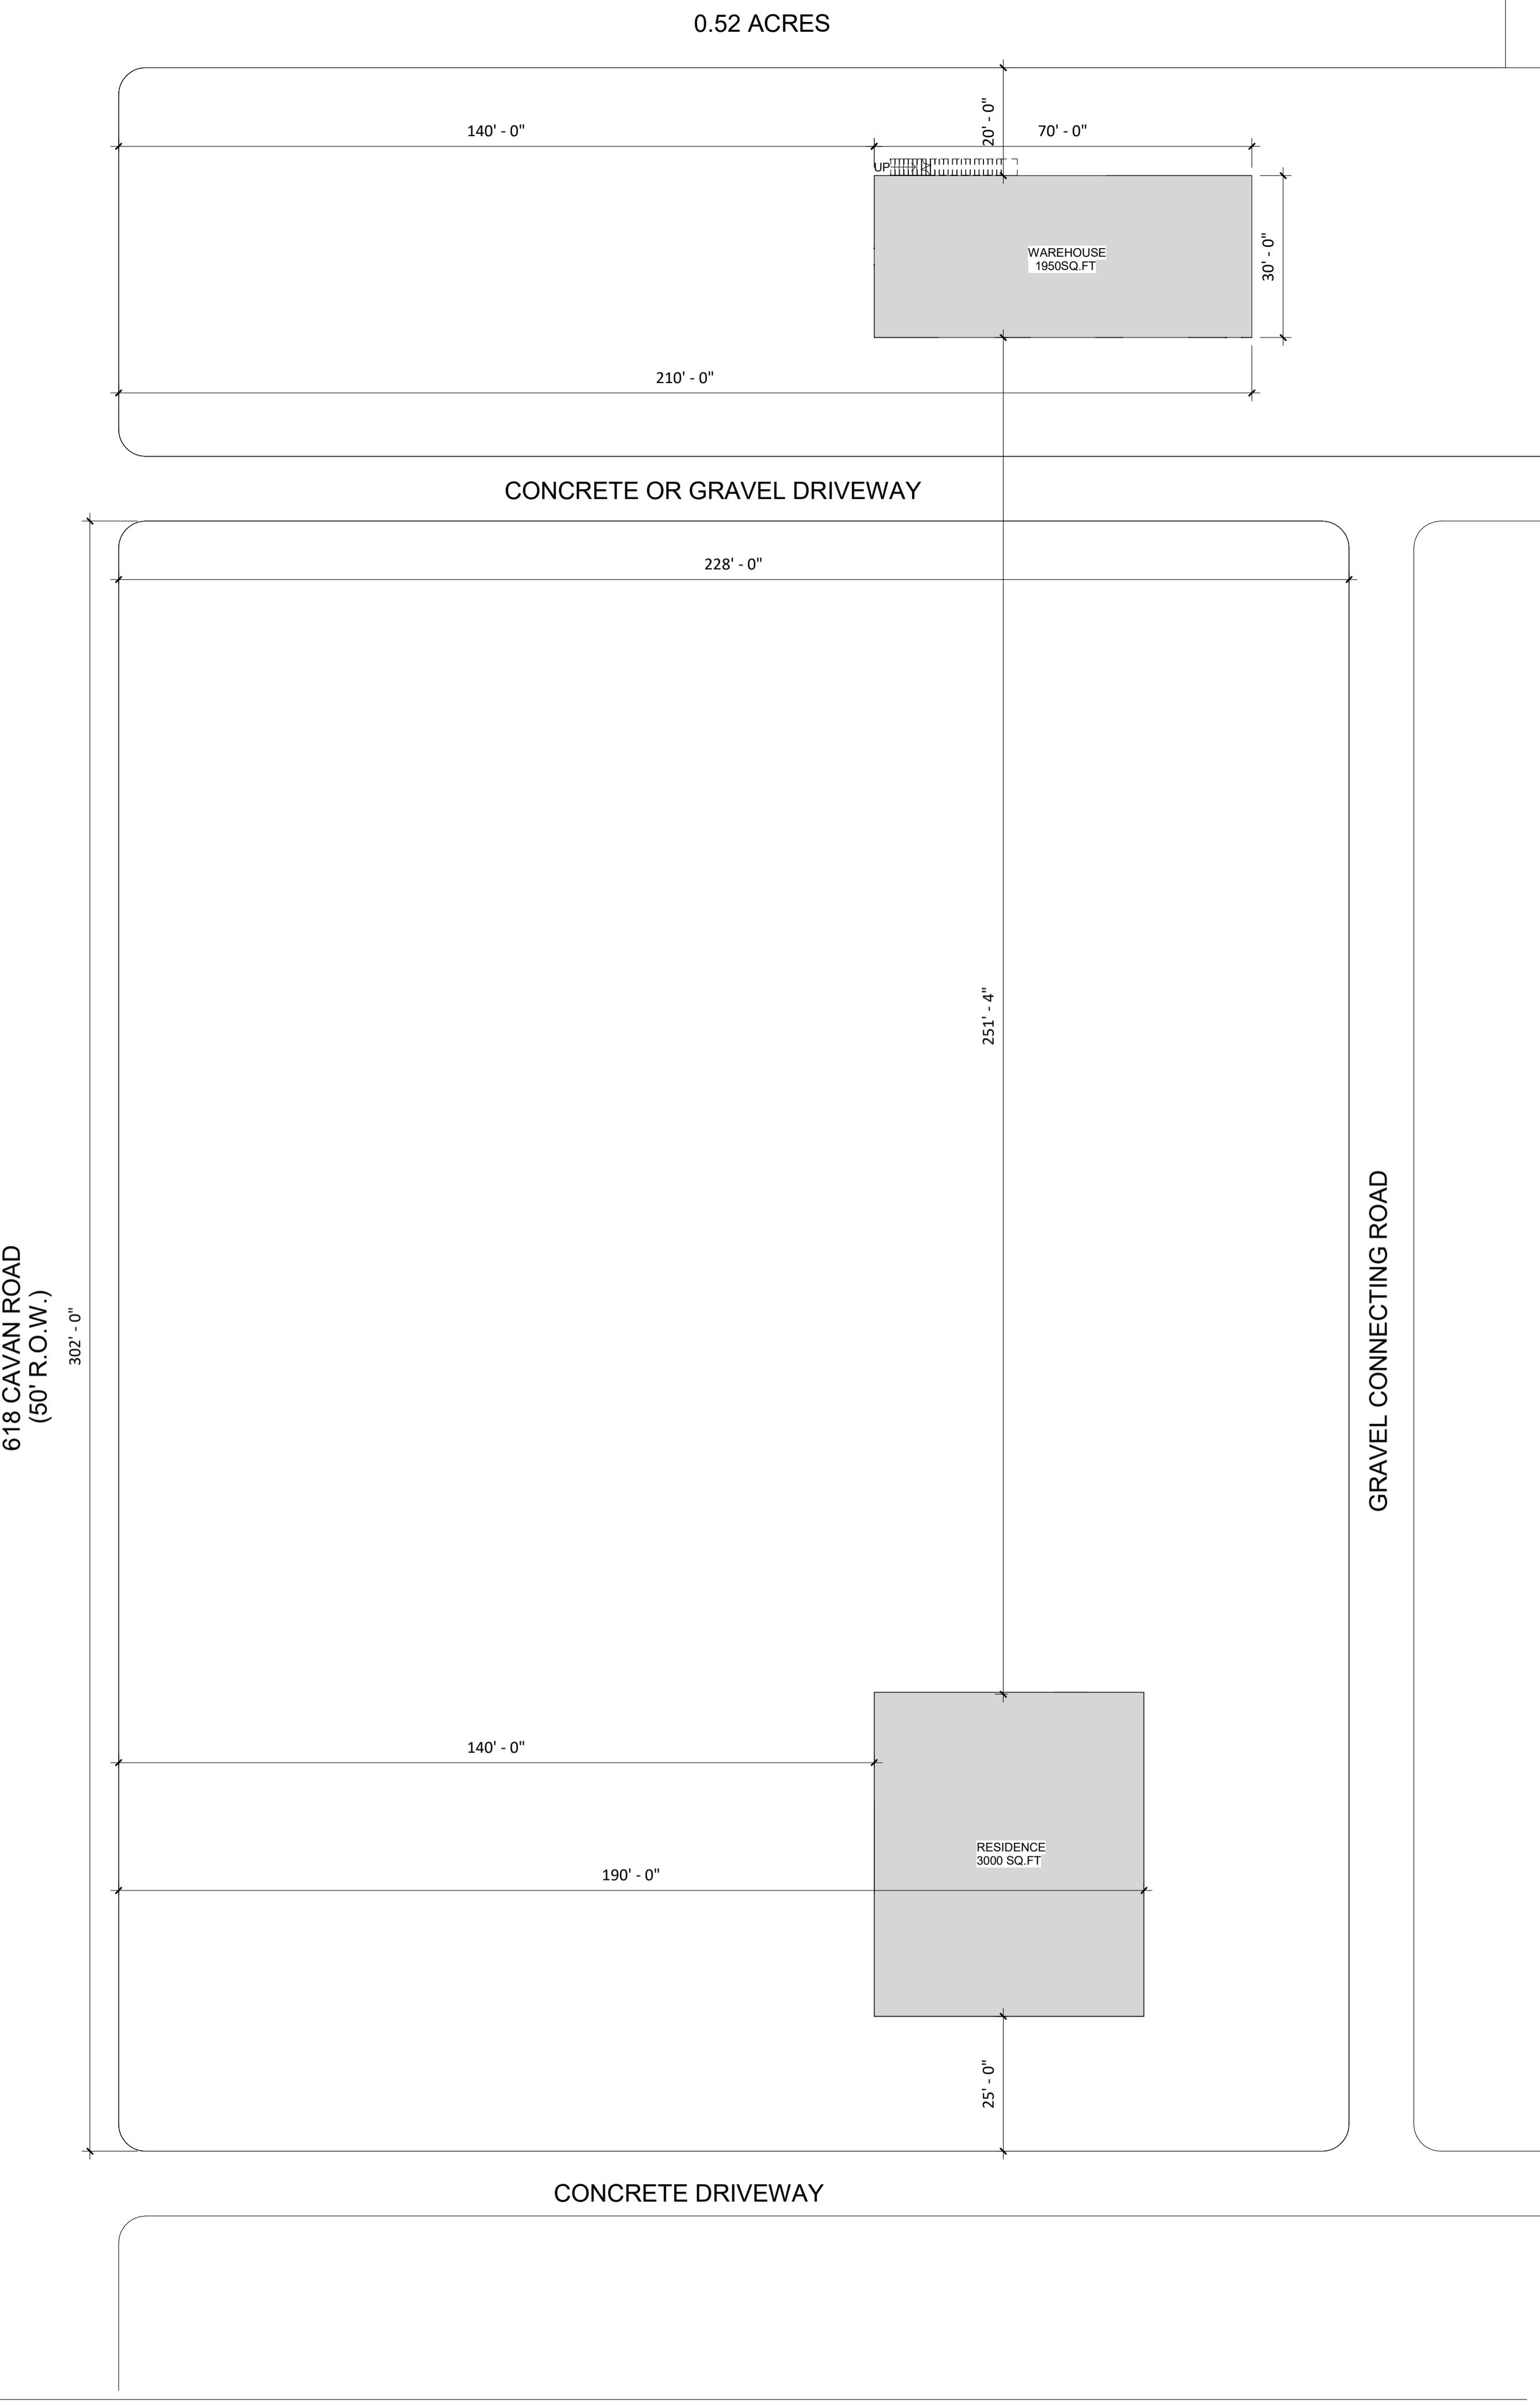


**SITE PLAN**  
1/16" = 1'-0"

## WINDOW SCHEDULE

TYPE	COUNT	HEIGHT	WIDTH	Manufacturer
W1	12	7' - 0"	3' - 0"	
Grand total: 12				

### Grand tot

## ISSUES

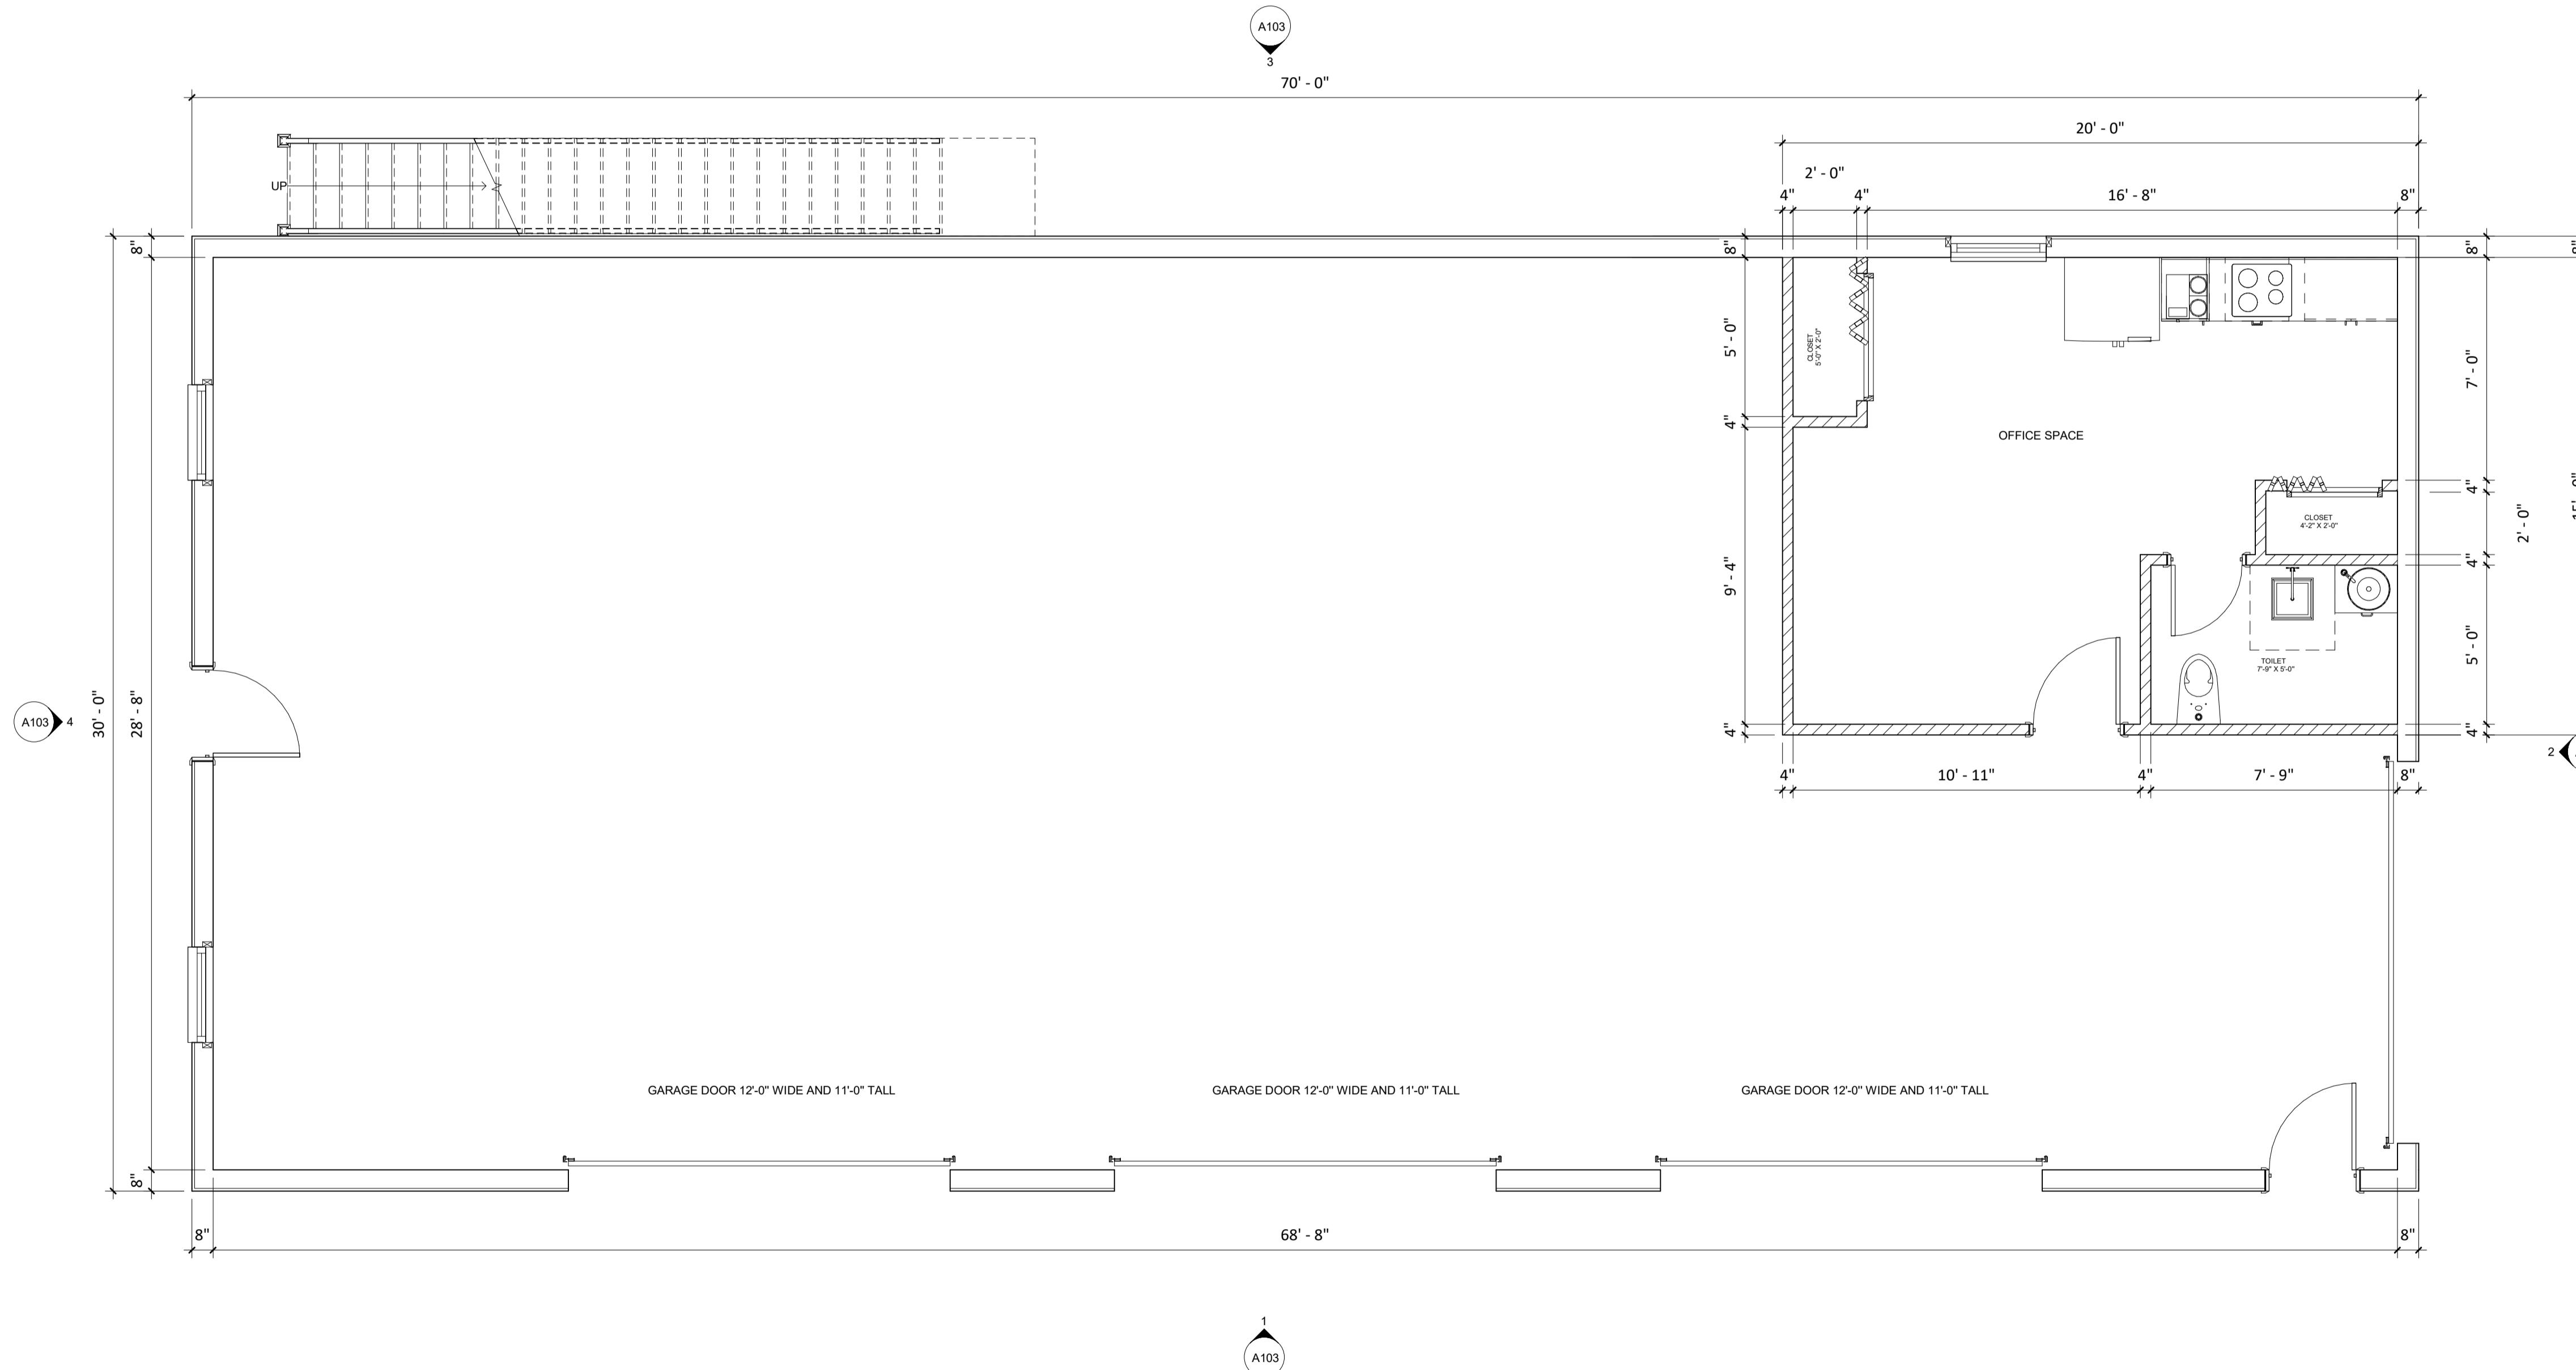

1  
A103

OWNER

<b>JOB NO.</b>	
<b>DATE</b>	
<b>DRAWN BY</b>	Author
<b>CHECKED BY</b>	Checker
<b>PHASE</b>	
<b>SHEET NAME</b>	
<b>WAREHOUSE FLOOR PLAN</b>	

SHEET NUMBER  
**A-100**

A102

CONTRACTOR  
KASSABILT LLC



ISSUES


NO.	DATE	DESCRIPTION

**LOT 6, BLOCK 31/1615 MOUNT AUBURN**

500/502 S GLASGOW DR. DALLAS, TX 75223

PARCEL ID: 00000166051000000

DALLAS COUNTY, TEXAS

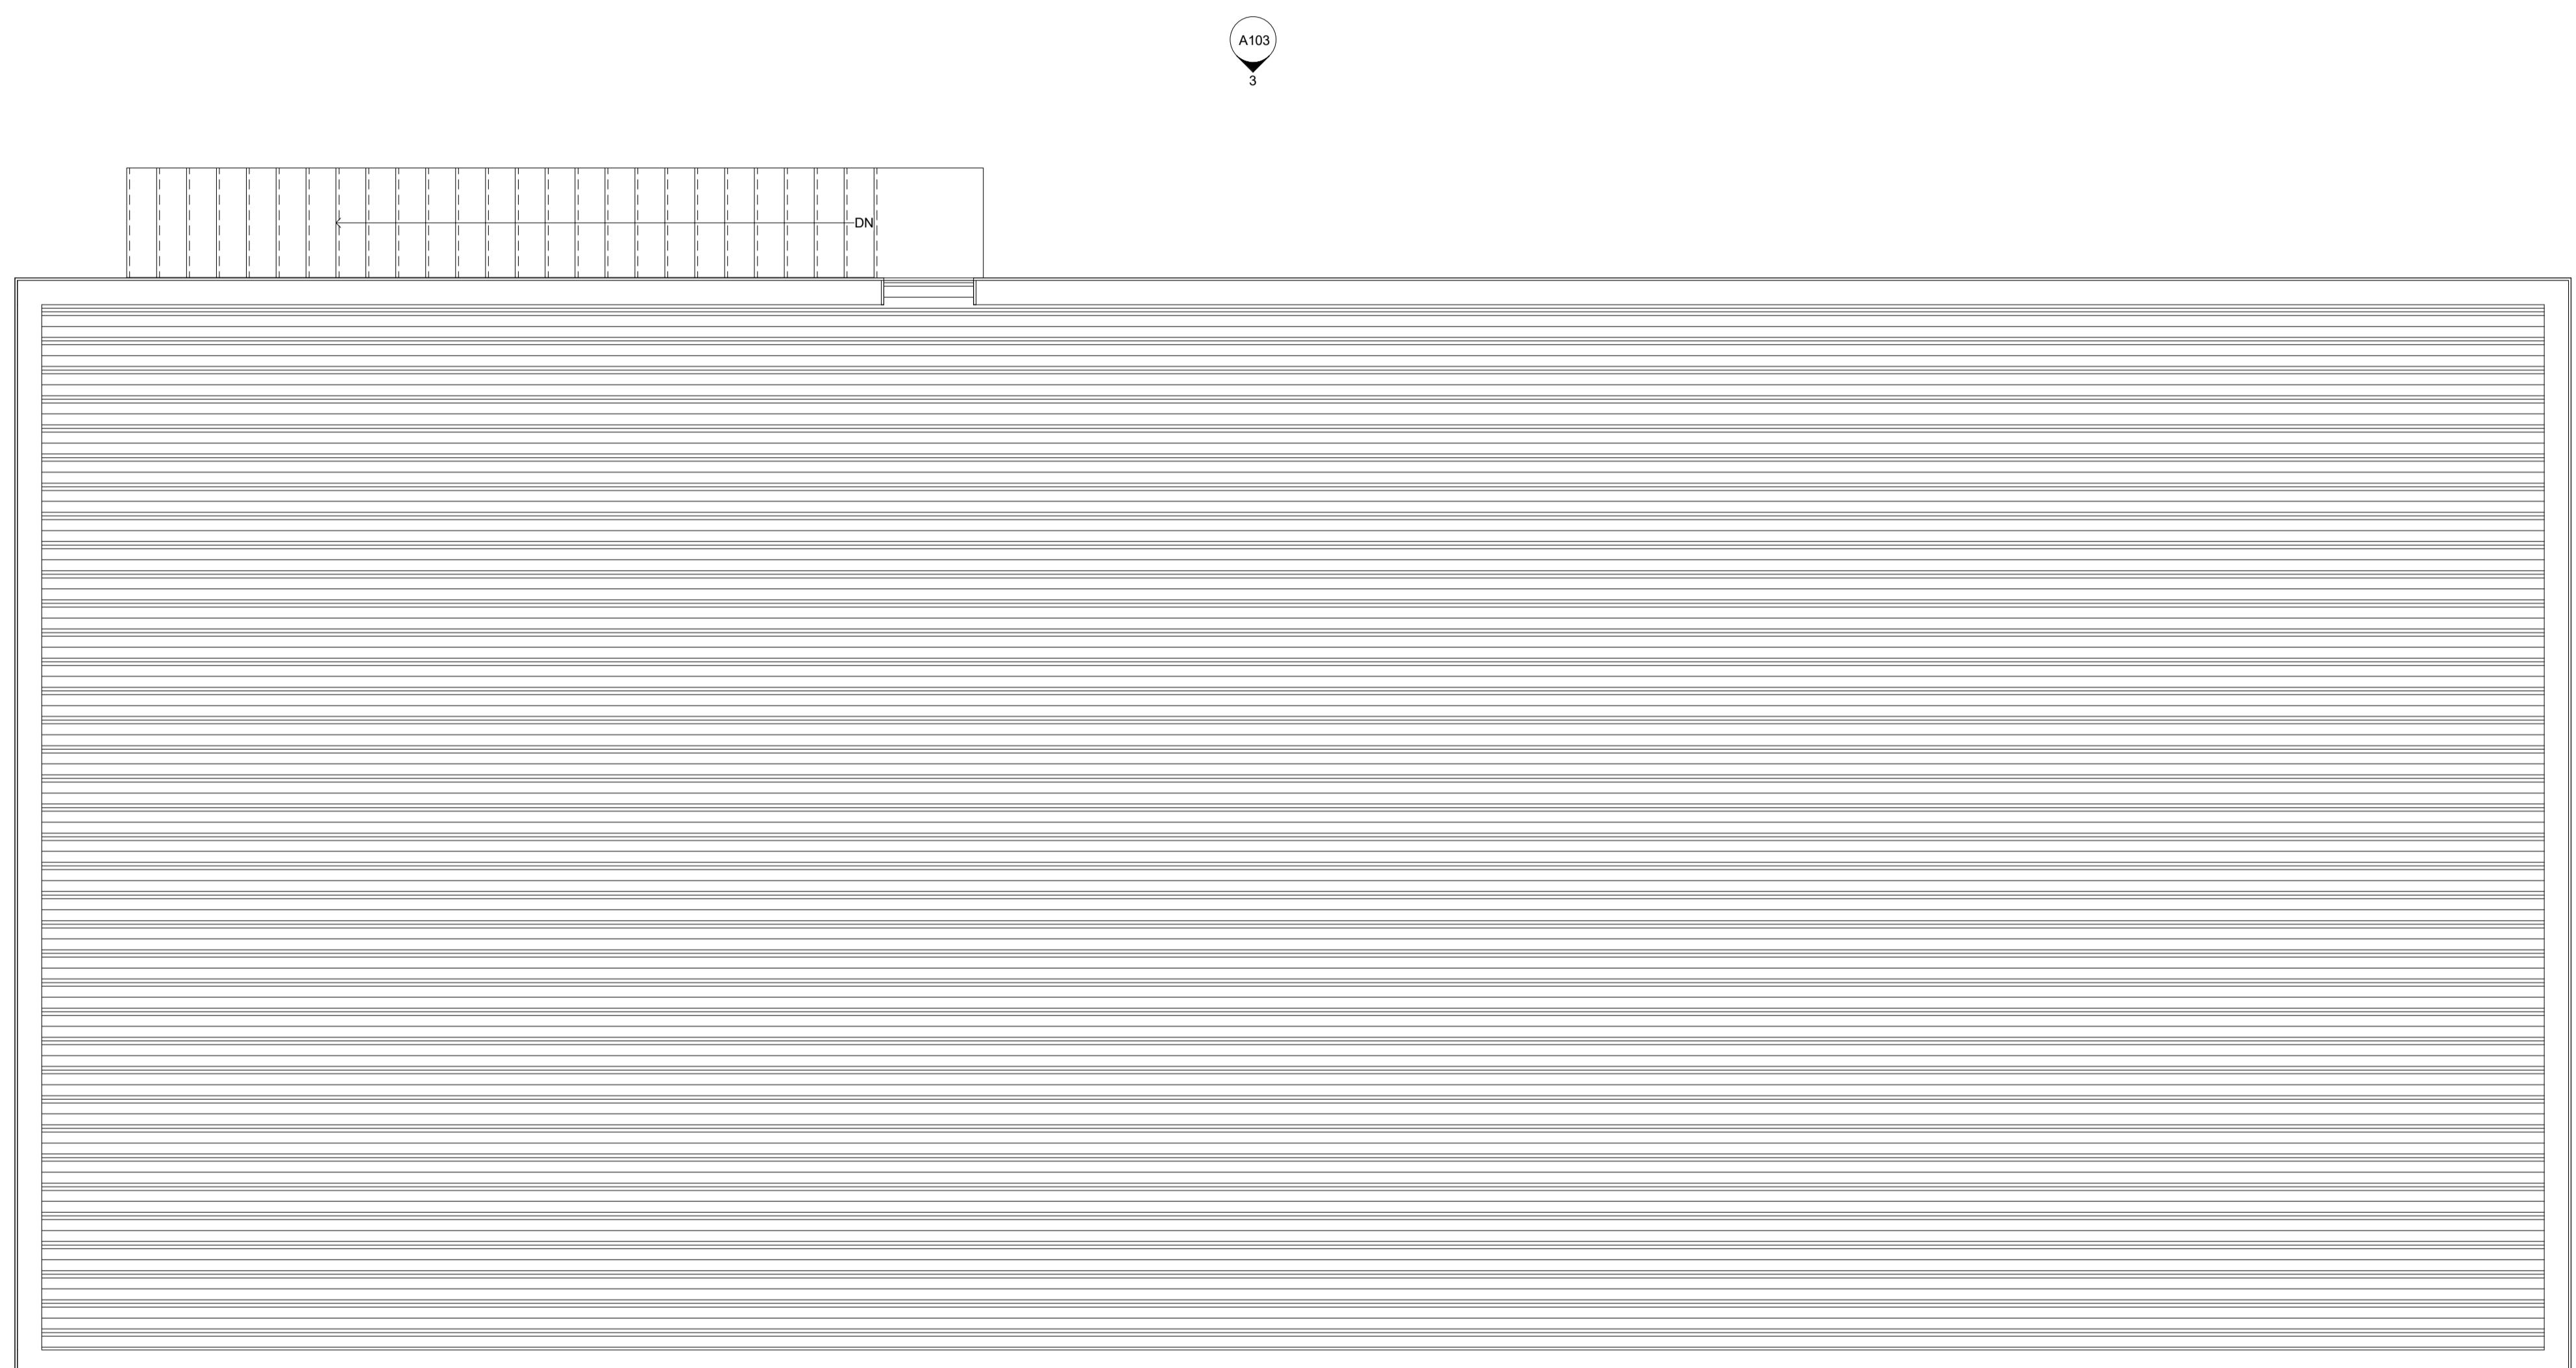

1

A103


Copyright (C) 2023 by KELLEY & KASSA COMMUNITIES LLC.  
All drawings, specifications and other documents prepared by the designer  
and/or architect for this project are the sole property of Kassabilt LLC  
solely with respect to this project and unless otherwise provided, Kassabilt  
LLC reserves all rights thereto. Any unauthorized copying or distribution  
of copies of architectural drawings, specifications and other documents  
is prohibited by law, statutory and other reserved rights, including the copyrights.  
Copies of architectural drawings, specifications and other documents  
for construction reference are prohibited unless expressly authorized by  
Kassabilt LLC in writing.

**OWNER**  
KELLEY & KASSA COMMUNITIES LLC - SERIES 1  
500/502 S GLASGOW DR.DALLAS, TX 75223

**JOB NO.** \_\_\_\_\_  
**DATE** 08/01/2024  
**DRAWN BY** \_\_\_\_\_ / Author  
**CHECKED BY** \_\_\_\_\_ / Checker  
**PHASE** \_\_\_\_\_  
**SHEET NAME** WAREHOUSE ROOF PLAN

**SHEET NUMBER** A102A

CONTRACTOR  
KASSABILT LLC

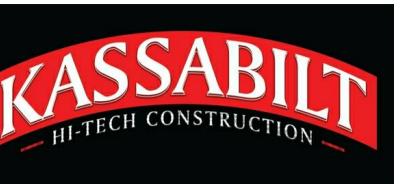

ISSUES


NO.	DATE	DESCRIPTION

**LOT 6, BLOCK 31/1615 MOUNT AUBURN**


500/502 S GLASGOW DR. DALLAS, TX 75223

PARCEL ID: 00000166051000000


DALLAS COUNTY, TEXAS

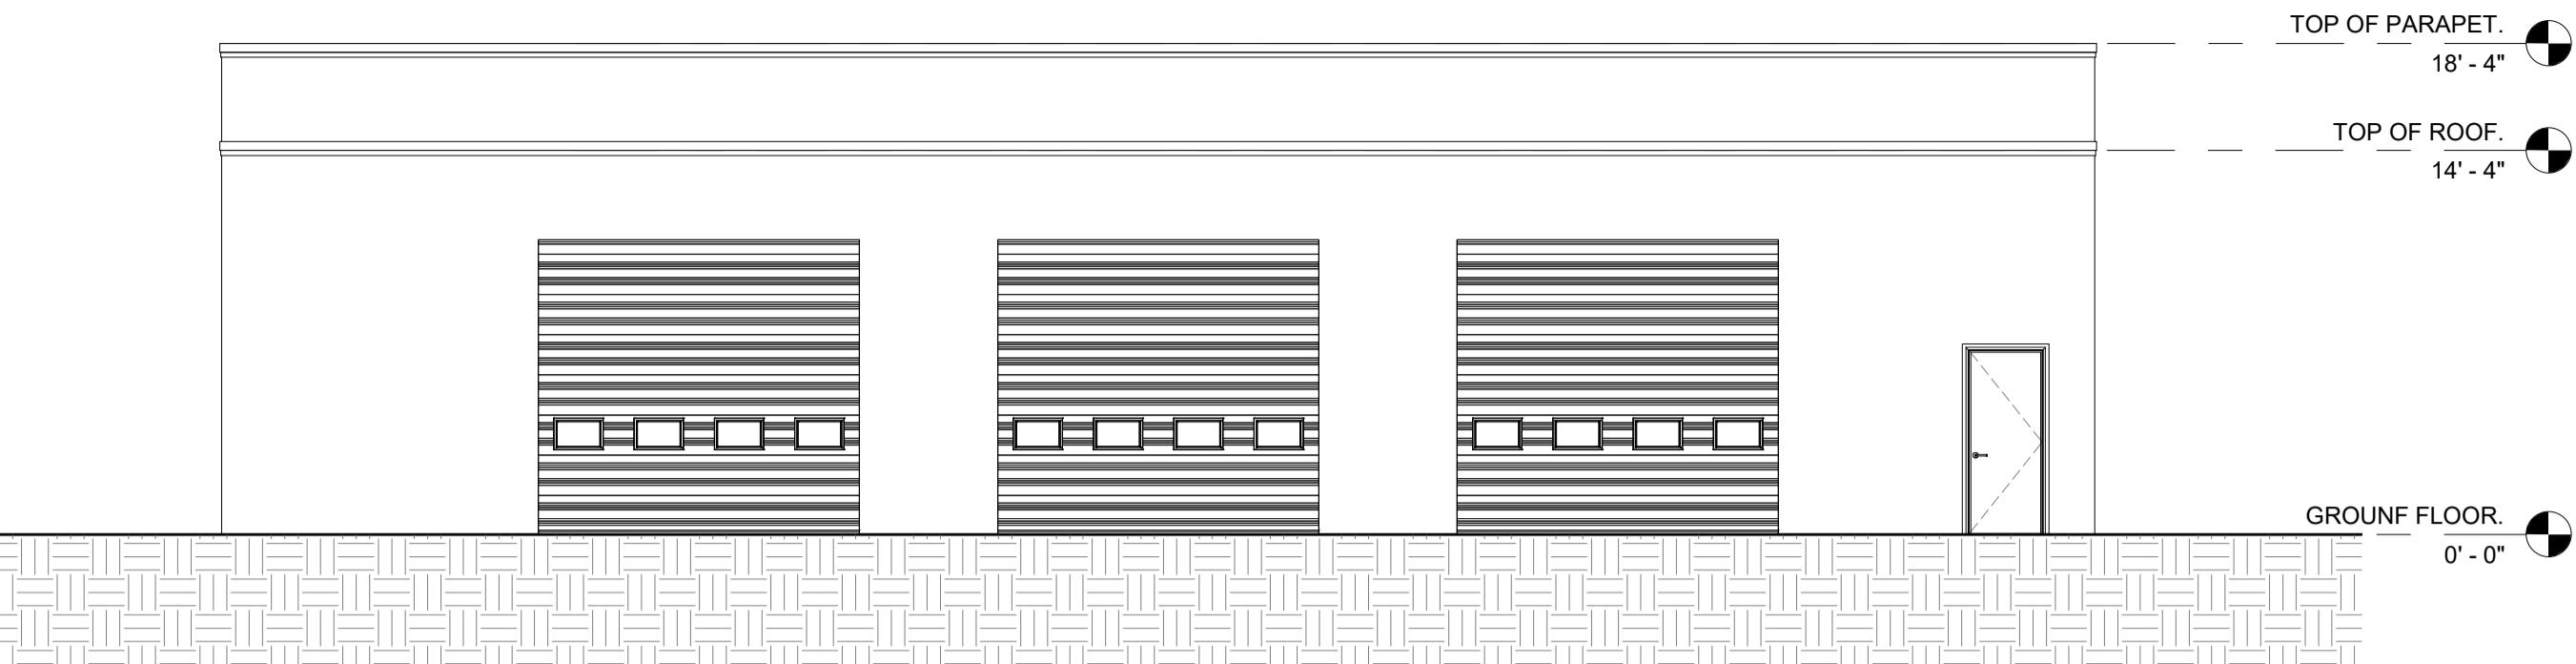


**1 WAREHOUSE ELEVATION - 1**  
3/16" = 1'-0"

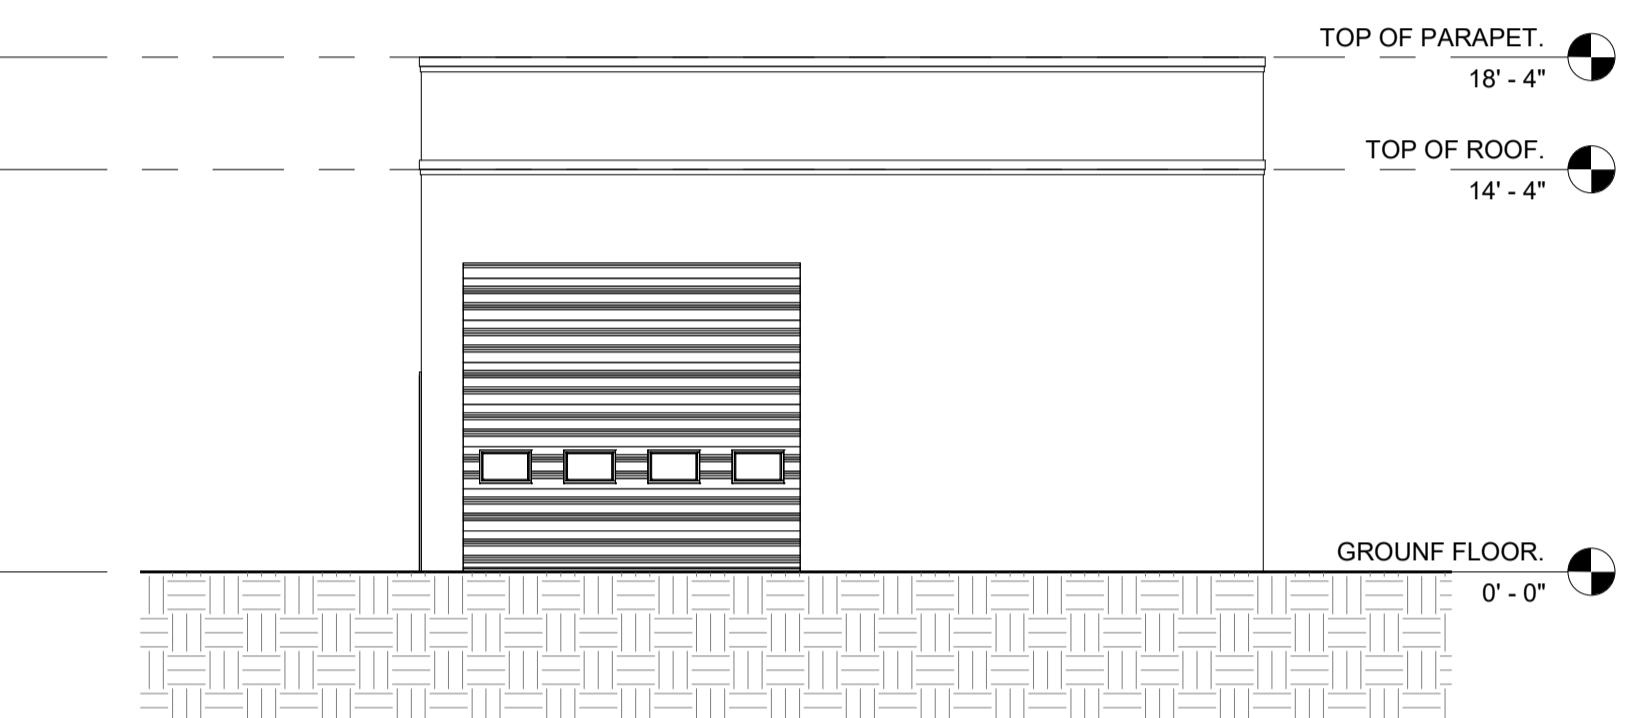

**2 WAREHOUSE ELEVATION - 2**  
3/16" = 1'-0"

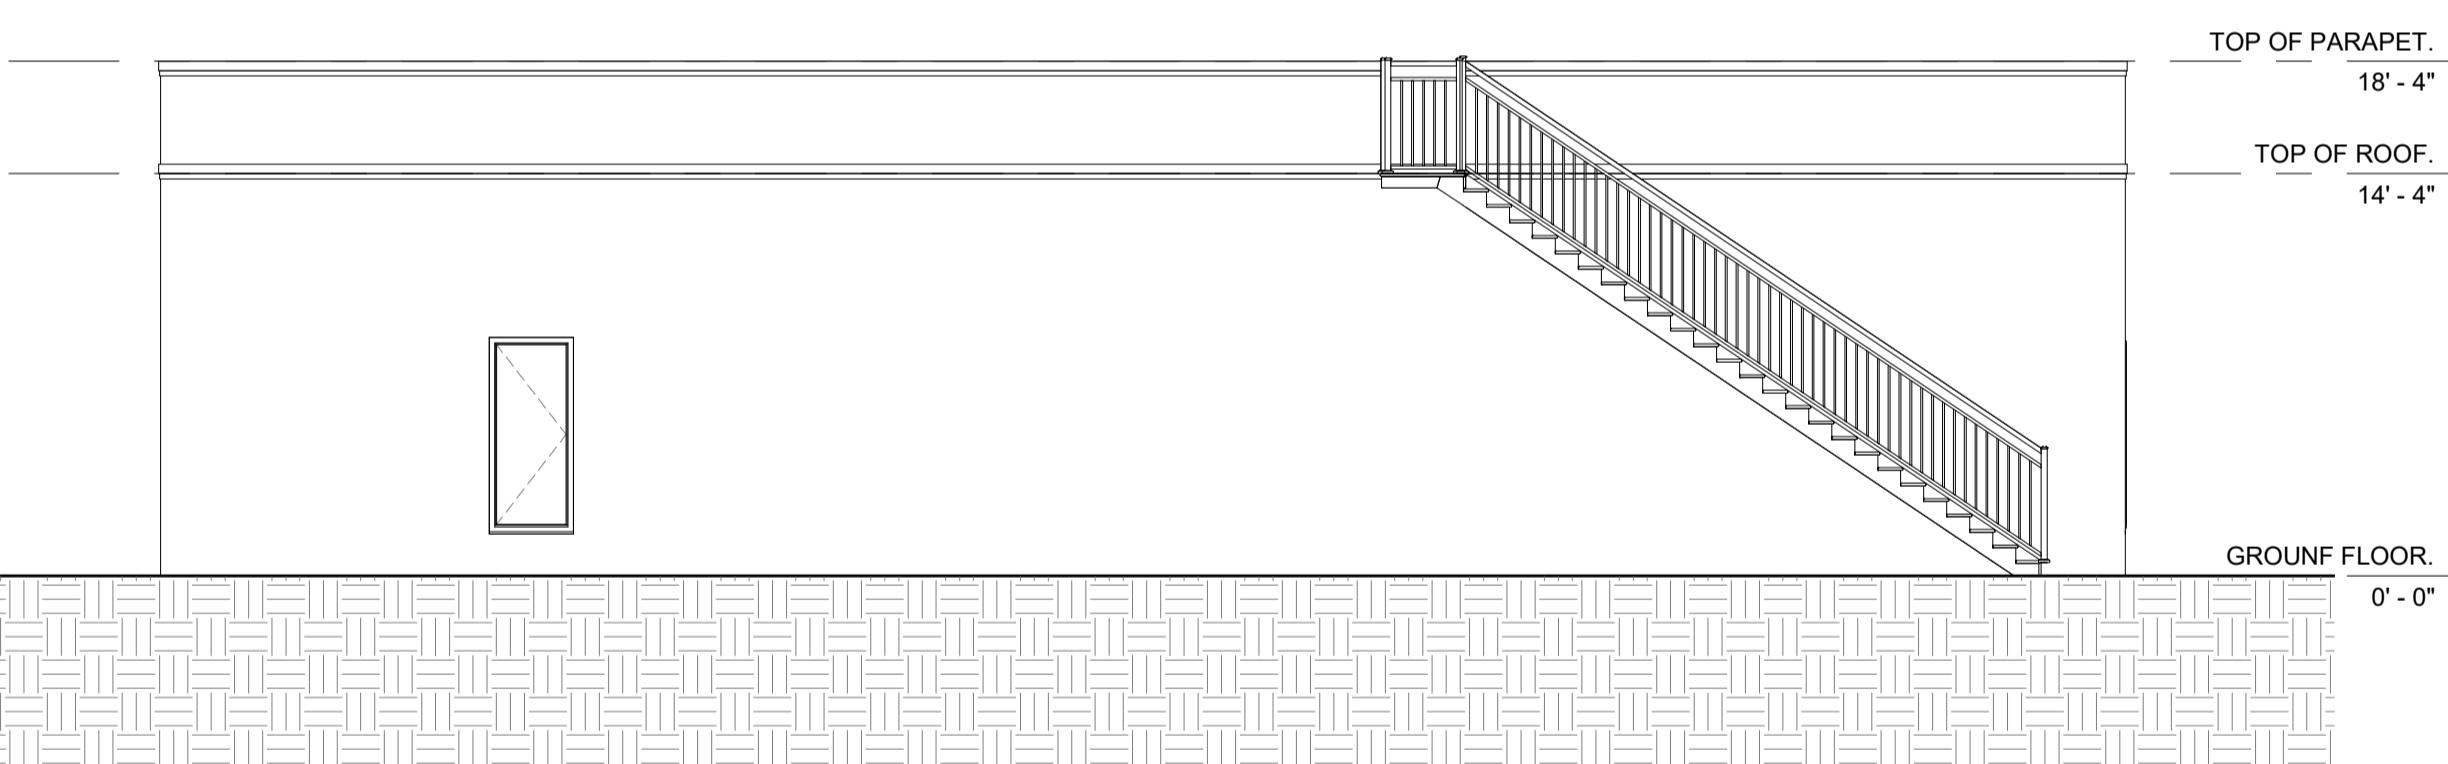

**3 WAREHOUSE ELEVATION - 3**  
3/16" = 1'-0"

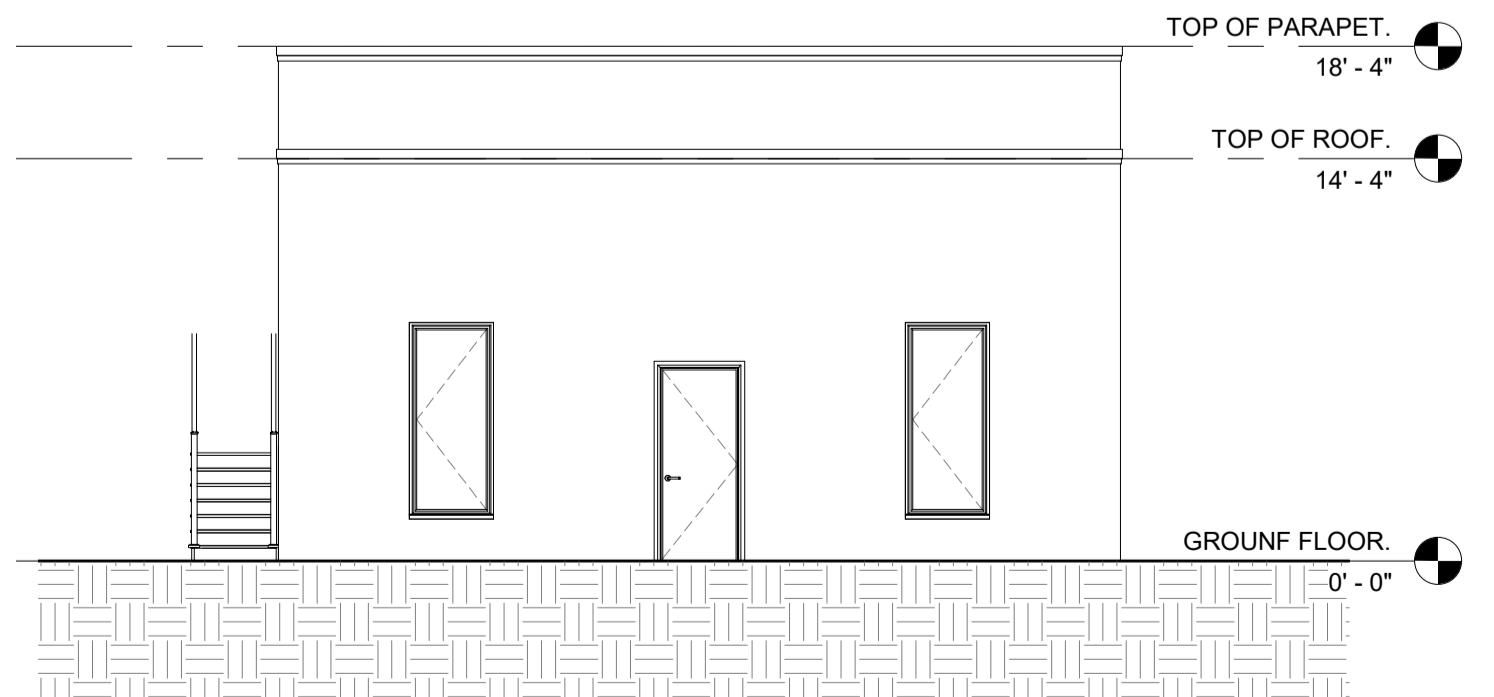


**4 WAREHOUSE ELEVATION - 4**  
3/16" = 1'-0"

Copyright (C) 2023 by KELLEY & KASSA COMMUNITIES LLC.  
All drawings, specifications and other documents prepared by the designer  
are the sole property of Kassabilt LLC and may not be reproduced or disclosed  
solely with respect to this project and unless otherwise provided, Kassabilt  
LLC reserves all rights, including all common law, statutory and other reserved rights,  
including the copyright.  
Copies of architectural drawings, specifications and other documents  
for information purposes are prohibited unless expressly authorized by  
Kassabilt LLC in writing.

**OWNER**  
KELLEY & KASSA COMMUNITIES LLC - SERIES 1  
500/502 S GLASGOW DR.DALLAS, TX 75223


**JOB NO.**  
**DATE** 08/01/2024  
**DRAWN BY** Author  
**CHECKED BY** Checker  
**PHASE**  
**SHEET NAME** WAREHOUSE ELEVATIONS

**SHEET NUMBER**  
**A103**

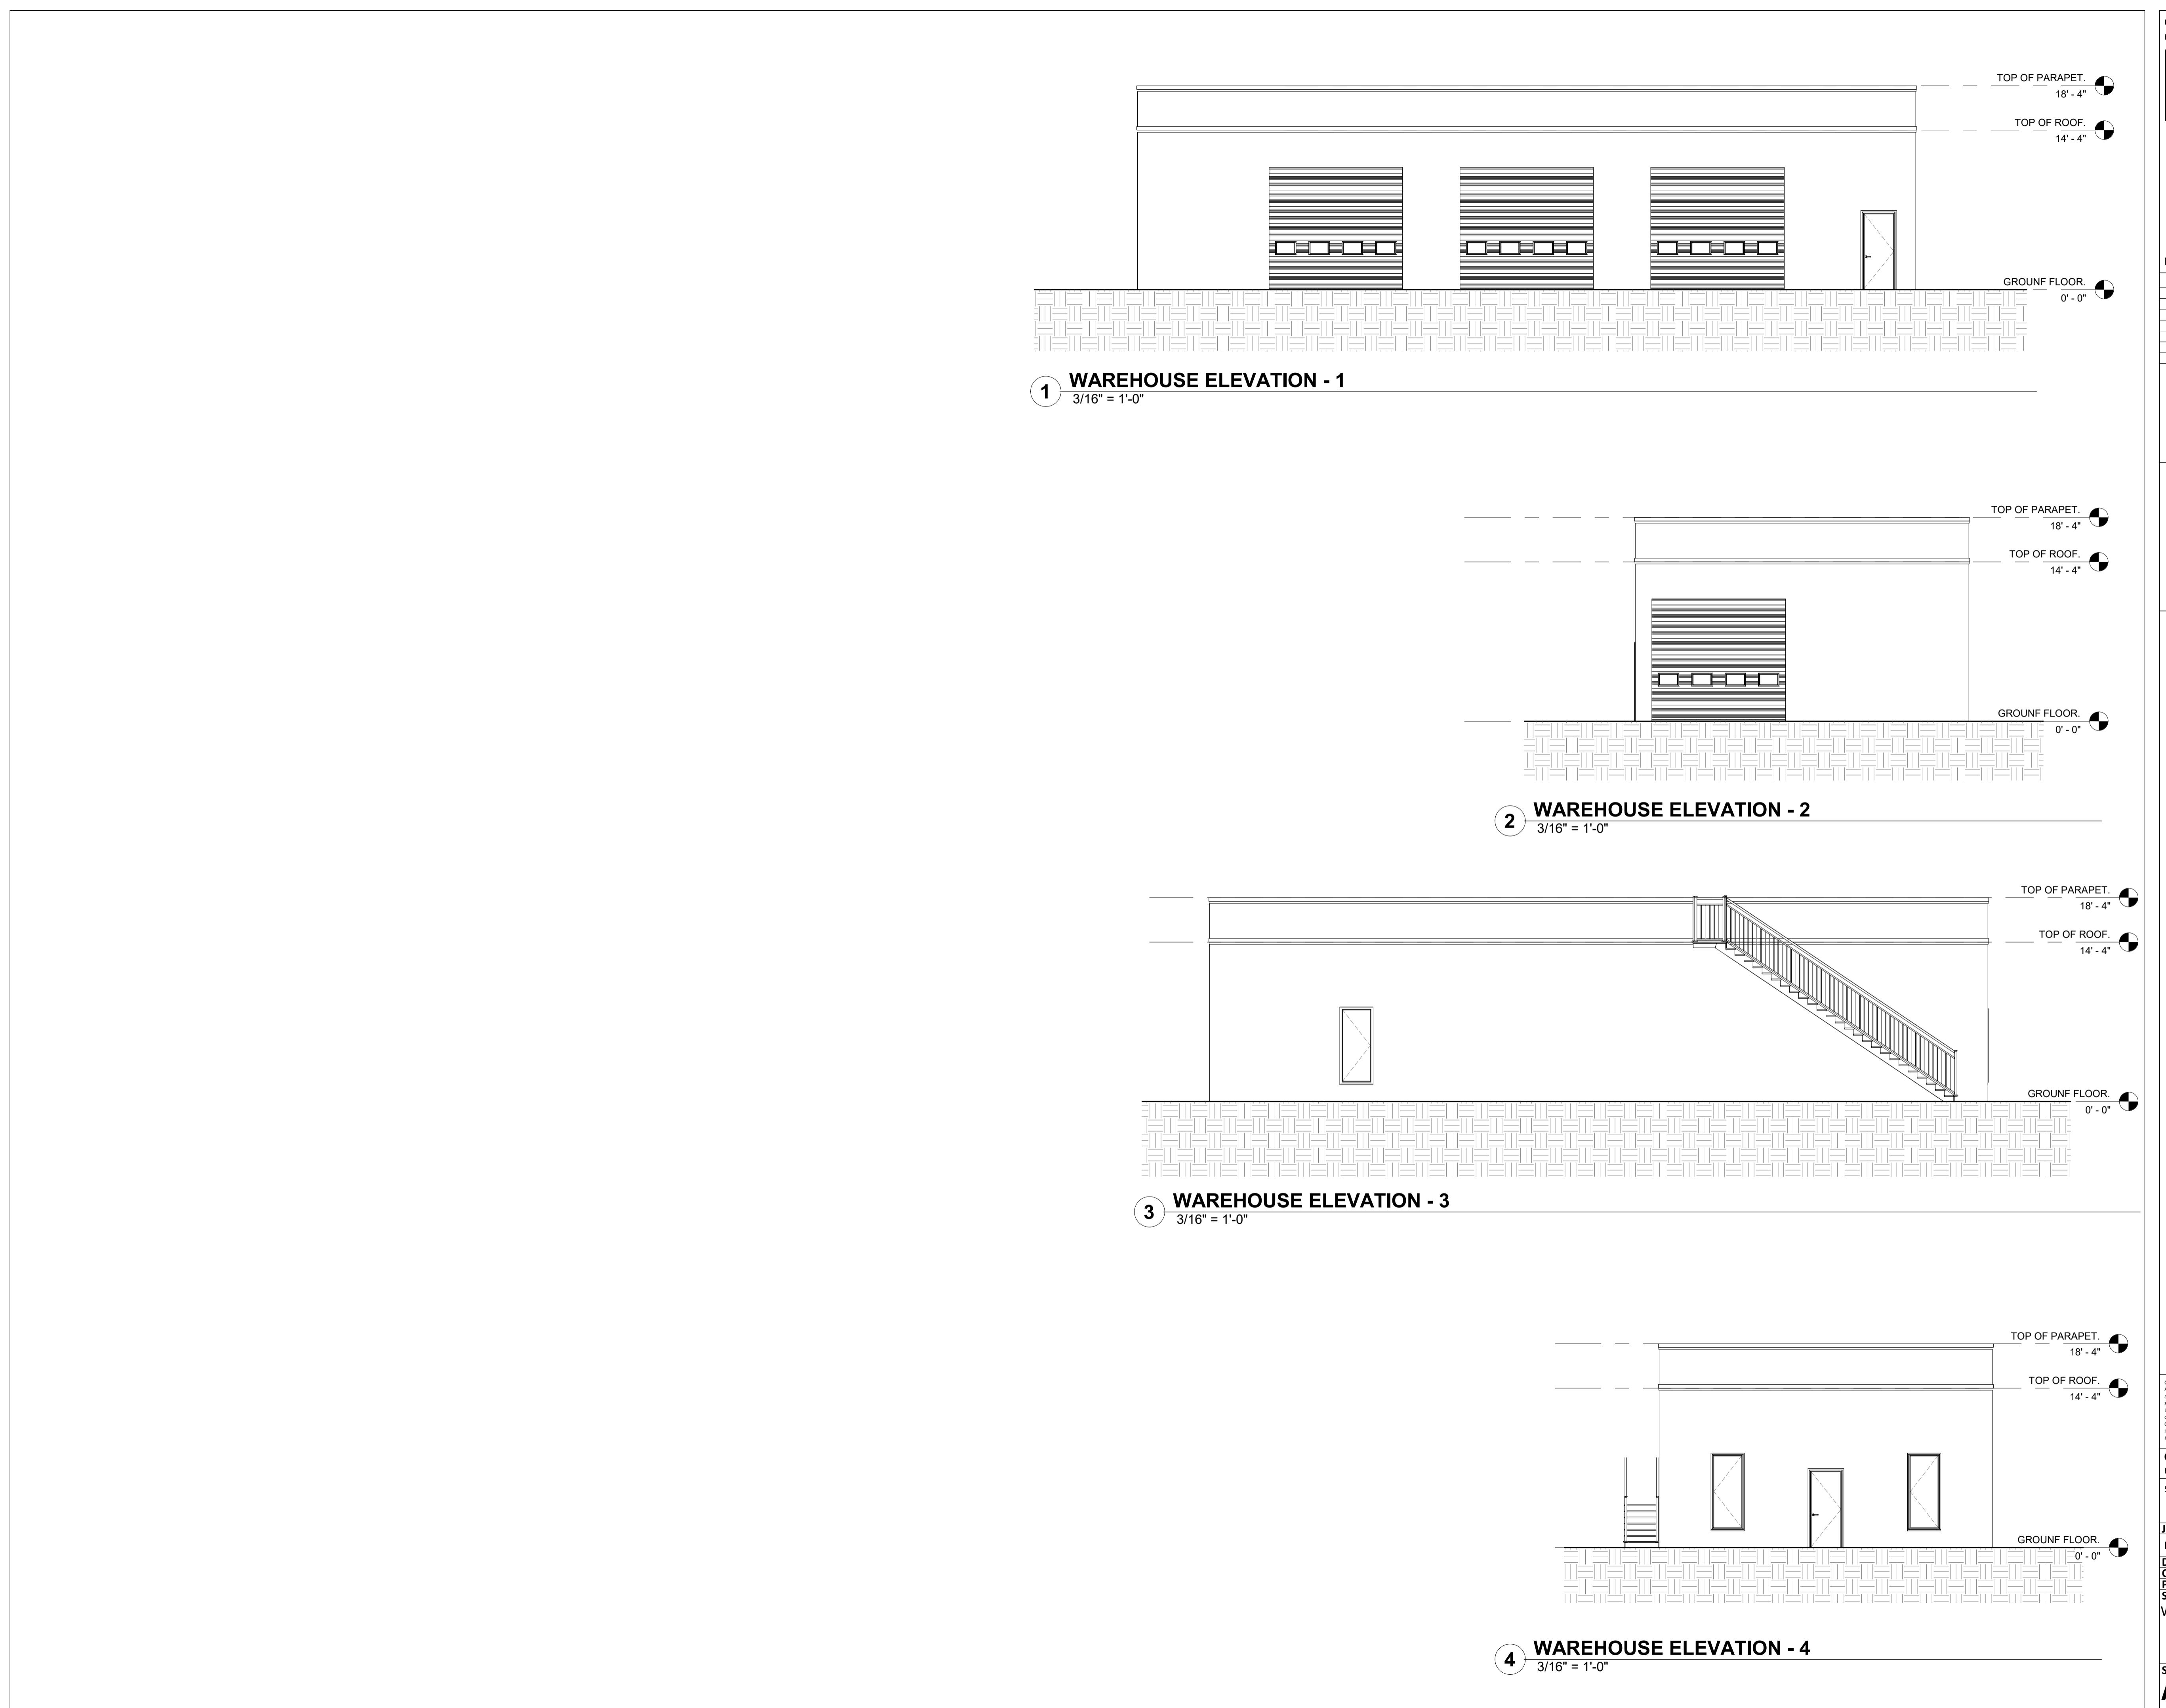

**TRACTOR  
BILT LLC**

ABILT LLC

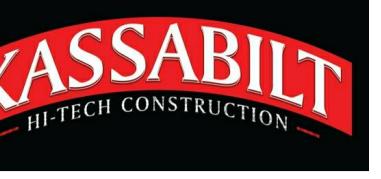


ES

500/500 S E1 ASSGOW DB DALLAS TX 75223

500/502 S GLASGOW DR. DALLAS, TX 75223

PARCEL ID: 00000166051000000

卷之三

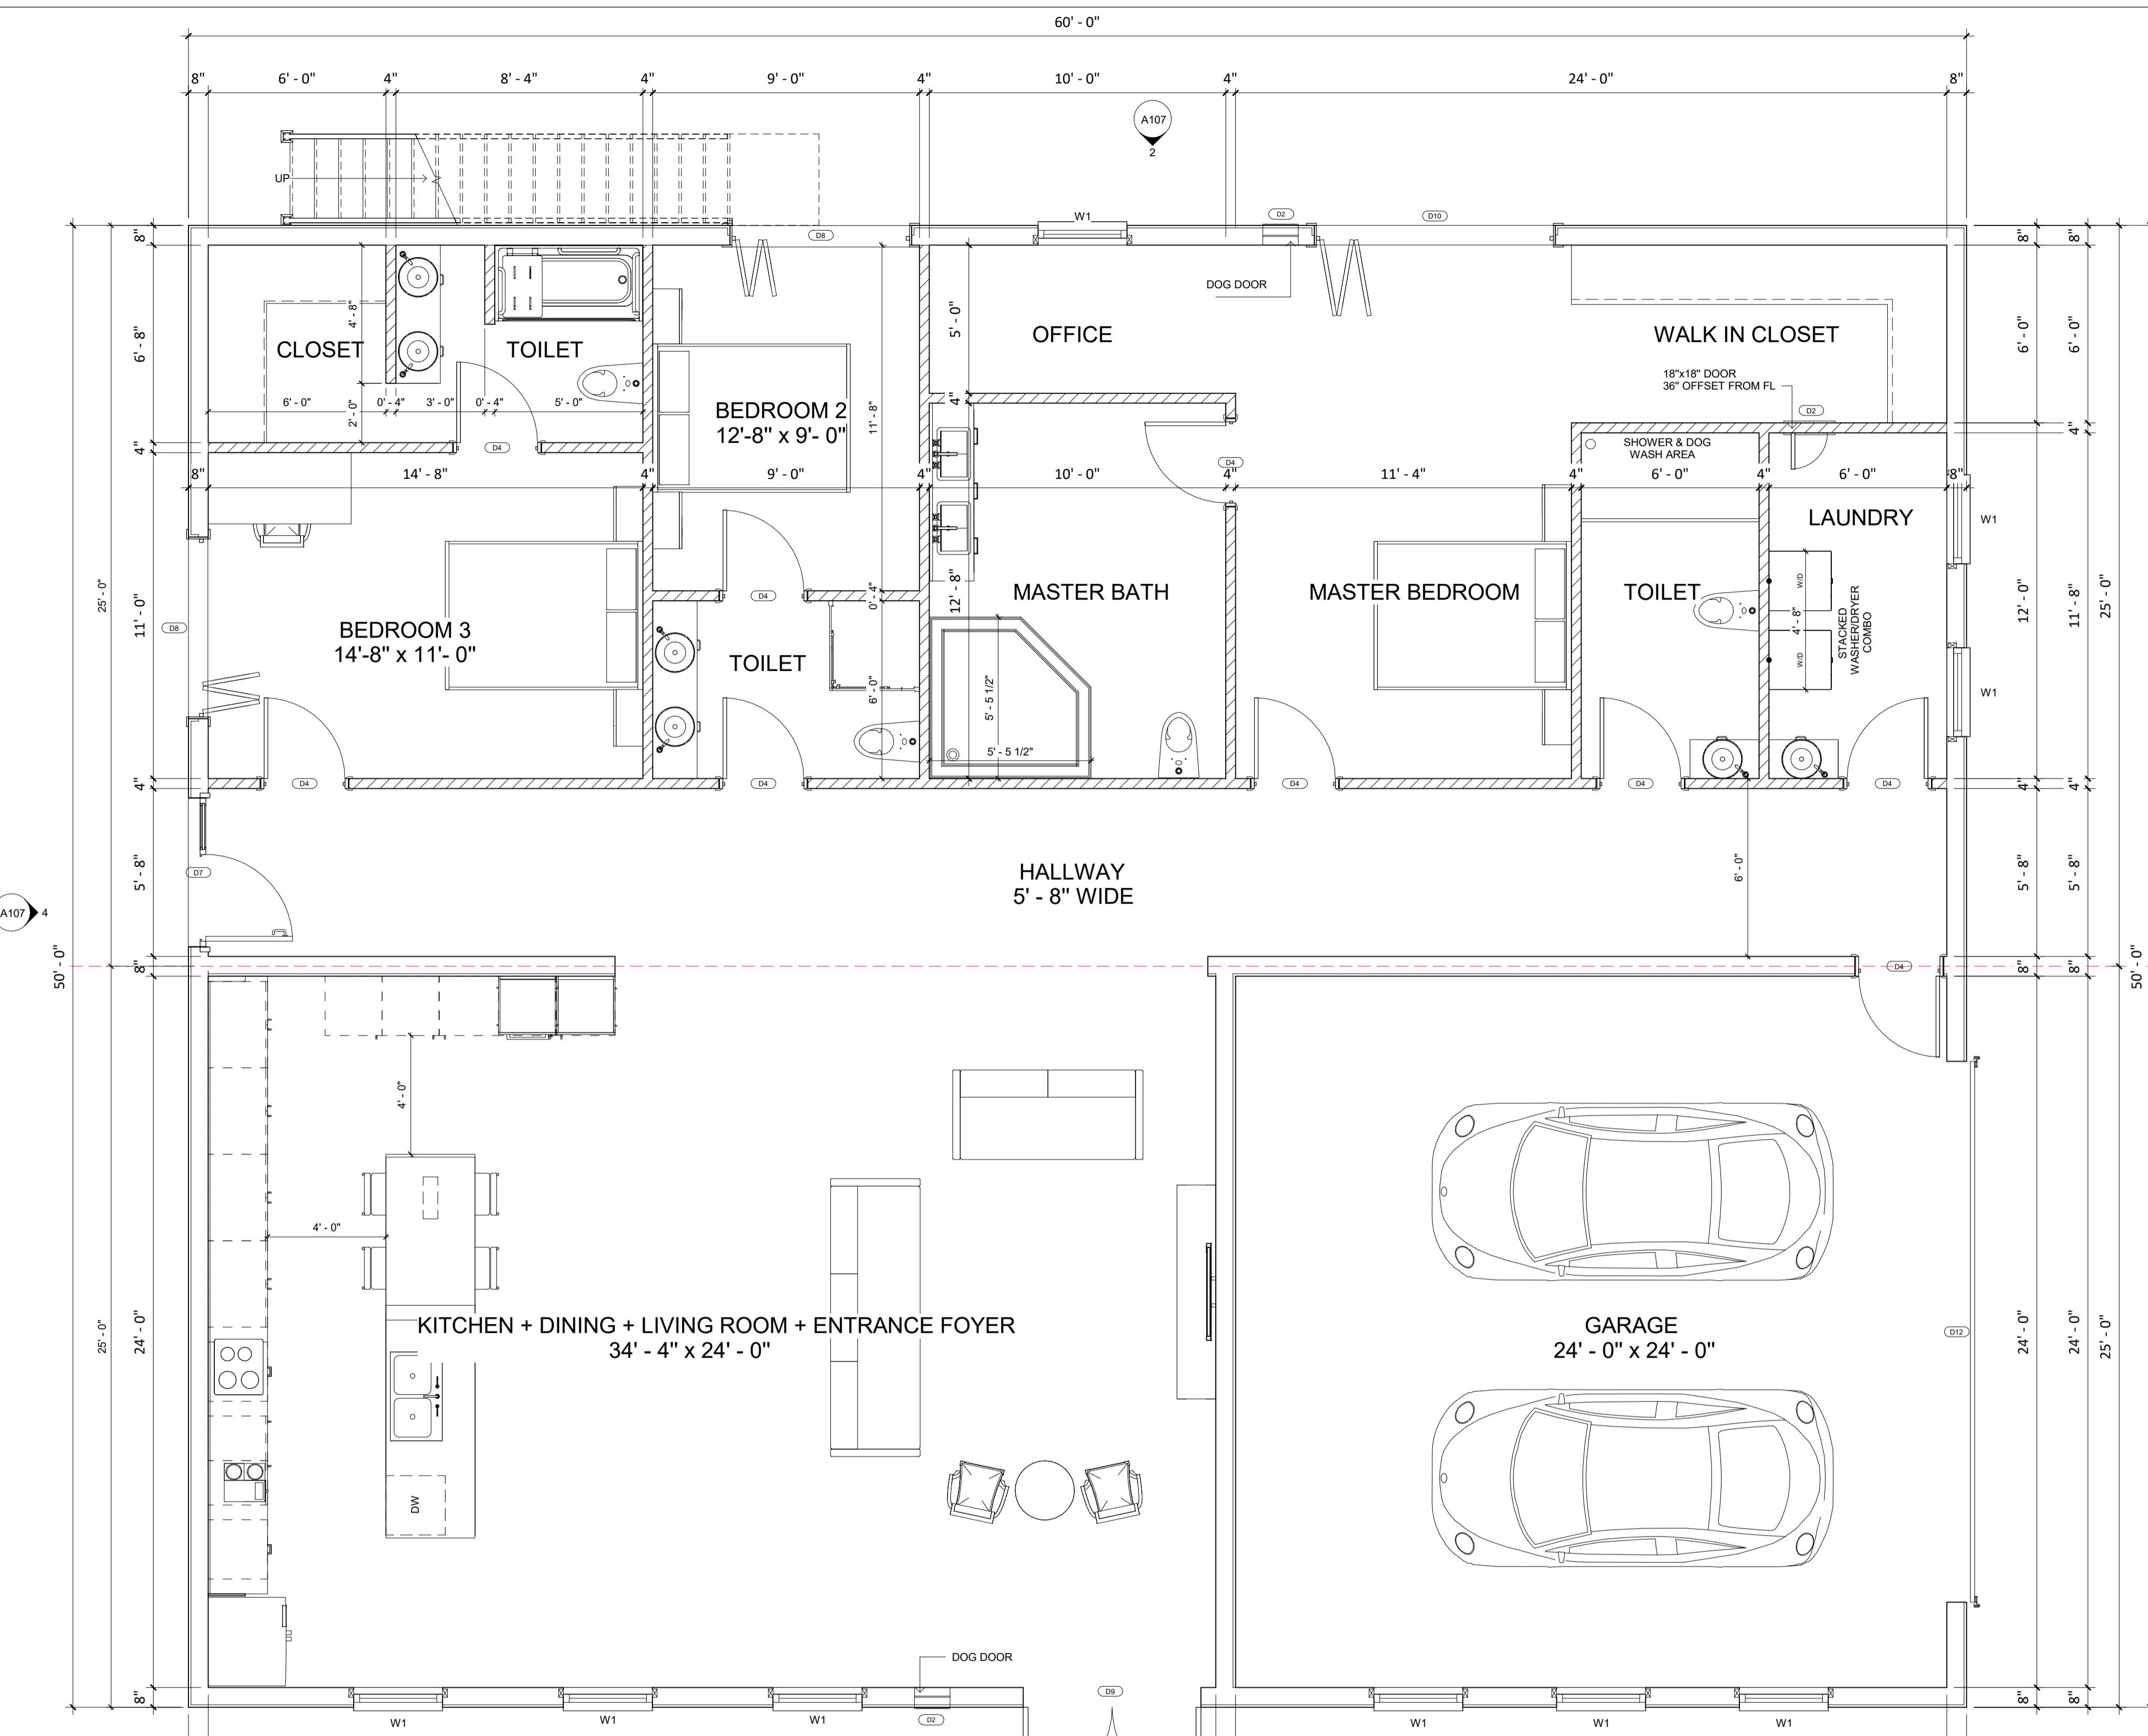

# 1 GROUND FLOOR PLAN

3/8" = 1'-0"

**1**   $3/8"$  =  $1'-0"$

WINDOW SCHEDULE				
Type	Count	Height	Width	Manufacturer
W1	13	7' - 0"	3' - 0"	
Grand total: 13				

DOOR SCHEDULE

Grand total: 28


(C) 2023 by KEILEY & KASSA COMMUNITIES LLC.  
All rights, specifications and other documents prepared by the designer  
and consultants for this project are instruments of Kassabilt LLC for use  
with respect to this project and unless otherwise provided, Kassabilt  
shall be deemed the author of these documents and shall retain all  
copyright, law, statutory and other reserved rights, including the copyrights.  
Architectural drawings, specifications and other documents for  
construction and reference are prohibited unless expressly authorized by  
KLLC in writing

NER  
Y & KASSA COMMUNITIES LLC - SERIES 1  
202 S GLASGOW DR DALLAS, TX 75223

NO.	
E	08/01/2024
WN BY	Author
CKED BY	Checker
SE	
T NAME	
USE GROUND FLOOR	
N	

**UNIT NUMBER  
104**

CONTRACTOR  
KASSABILT LLC

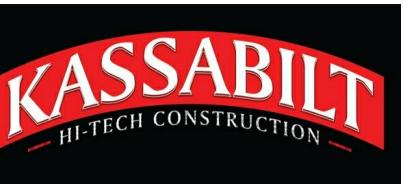

ISSUES


NO.	DATE	DESCRIPTION

**LOT 6, BLOCK 31/1615 MOUNT AUBURN**

500/502 S GLASGOW DR. DALLAS, TX 75223

PARCEL ID: 00000166051000000

DALLAS COUNTY, TEXAS

 

Copyright (C) 2023 by KELLEY & KASSA COMMUNITIES LLC.  
All drawings, specifications and other documents prepared by the designer  
are the sole property of KELLEY & KASSA COMMUNITIES LLC and are provided to Kassabilt  
solely with respect to this project and unless otherwise provided, Kassabilt  
shall not have the right to copy or otherwise utilize such drawings, specifications  
or other documents. Any unauthorized copying, reproduction, disclosure or use  
of such drawings, specifications and other documents is prohibited by law.  
Copies of architectural drawings, specifications and other documents by  
Kassabilt LLC in writing.

**OWNER**  
KELLEY & KASSA COMMUNITIES LLC - SERIES 1  
500/502 S GLASGOW DR.DALLAS, TX 75223

**JOB NO.** \_\_\_\_\_  
**DATE** 08/01/2024  
**DRAWN BY** \_\_\_\_\_ Author  
**CHECKED BY** \_\_\_\_\_ Checker  
**PHASE** \_\_\_\_\_  
**SHEET NAME** HOUSE ROOF LEVEL PLAN

**SHEET NUMBER** A104A

**1** ROOF LEVEL  
3/8" = 1'-0"

# TRACTOR BILT LLC

ABILITY LLC



# ISSUES


**LOT 6, BLOCK 31/1615 MOUNT AUBURN**

500/502 S GLASGOW DR. DALLAS, TX 75223


DAWSON COUNTY TEXAS




# **ELEVATION - 1**

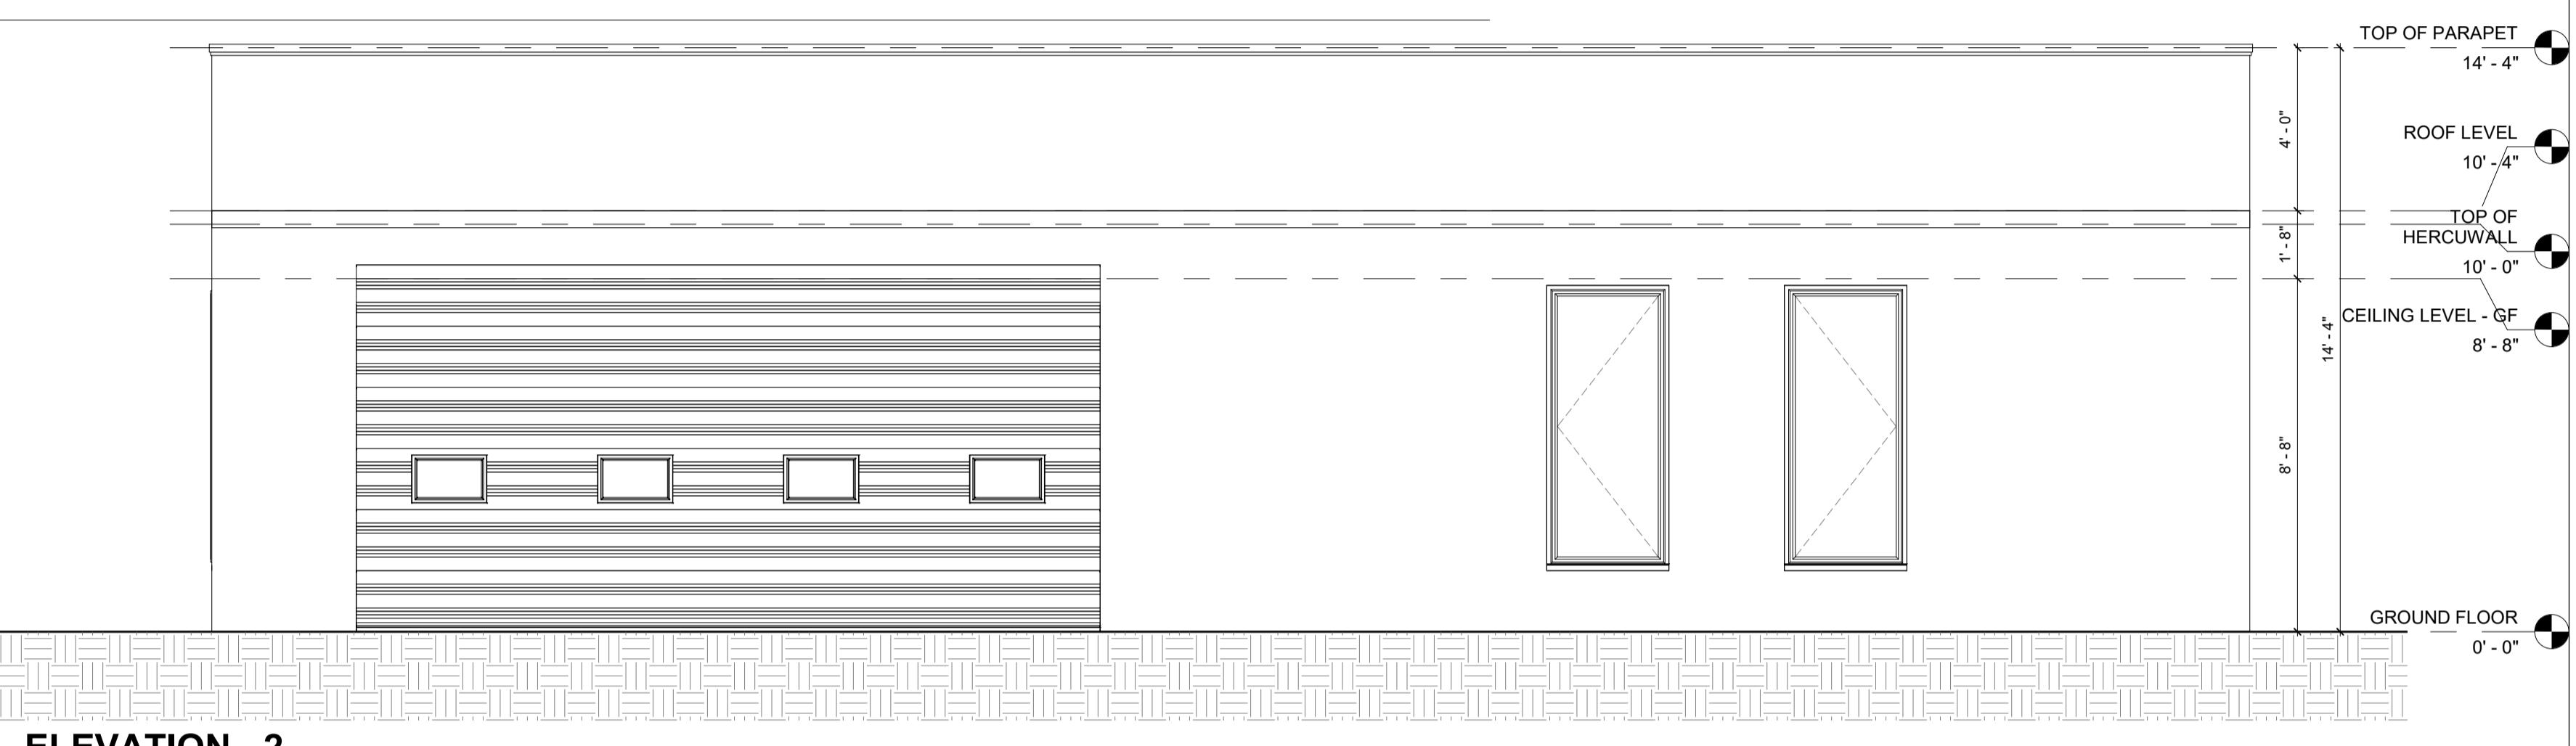

**3** ELEVATION - 2  
3/8" = 1'-0"

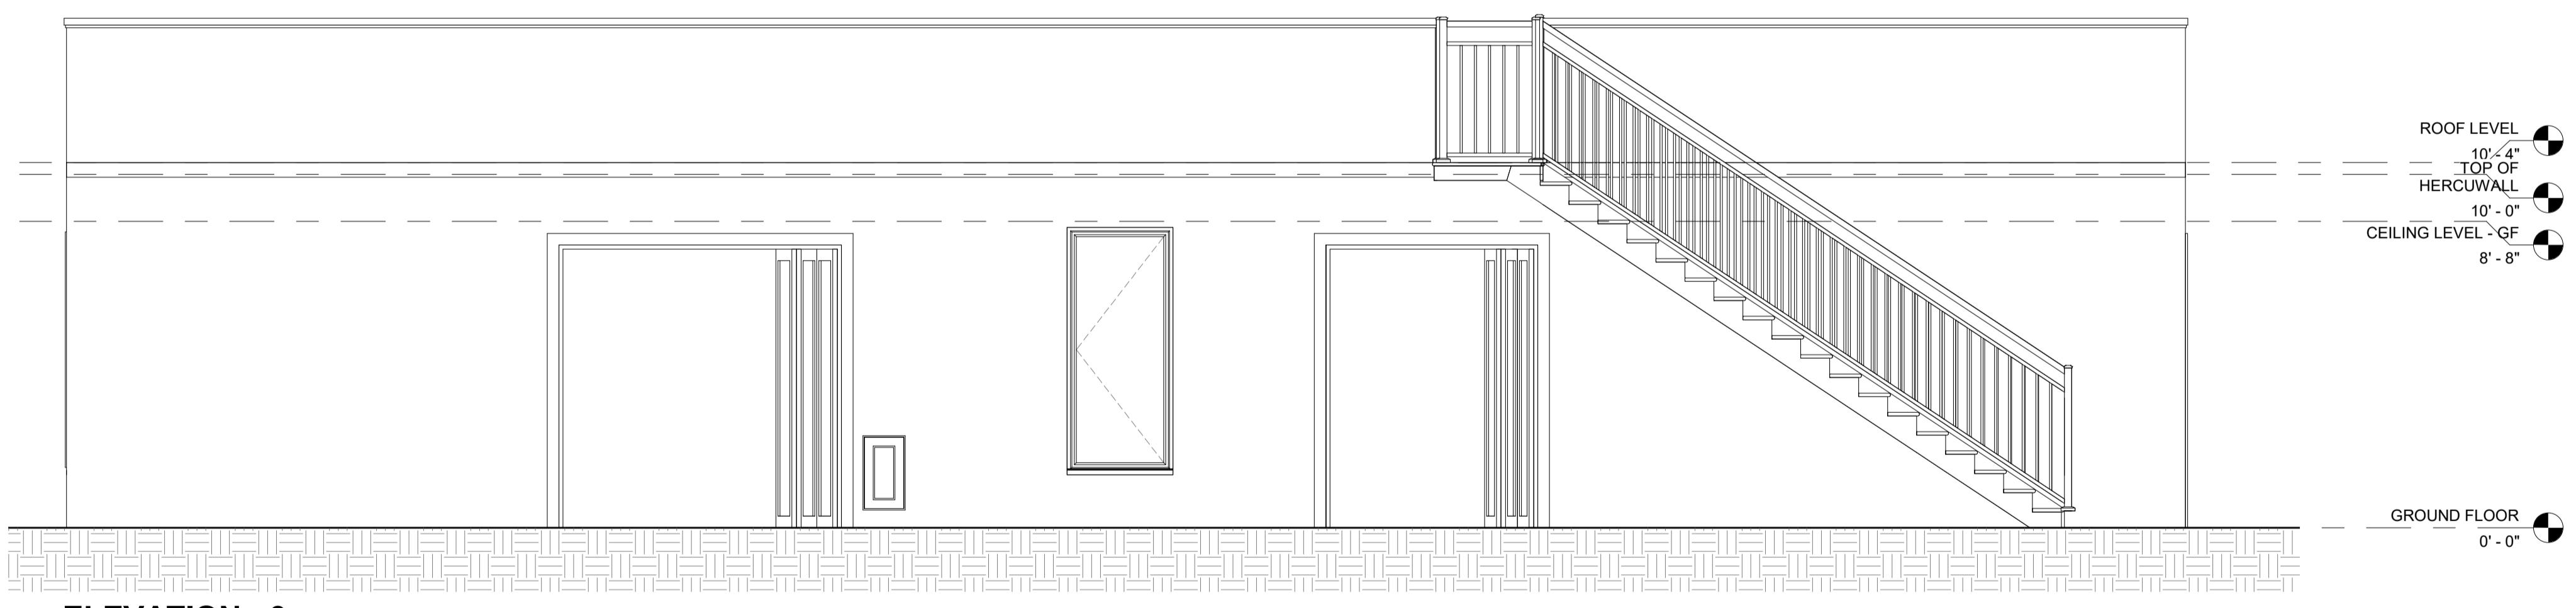

## **ELEVATION - 3**

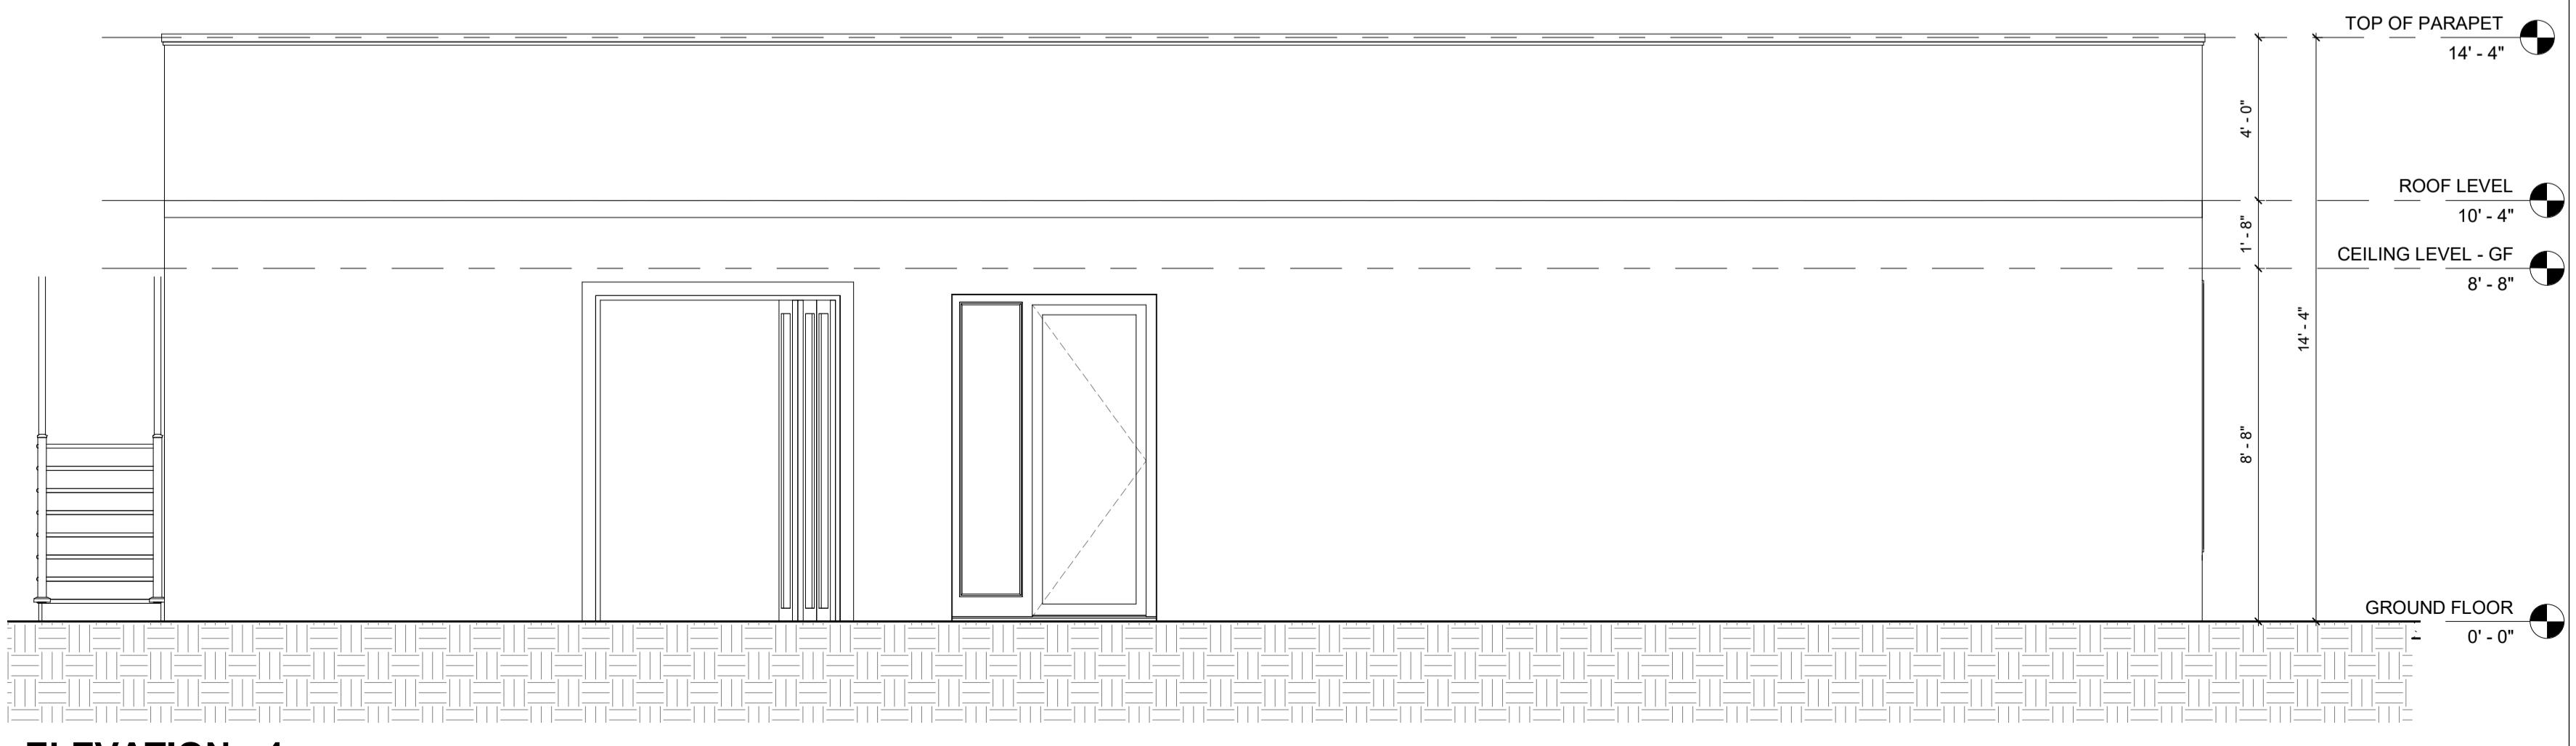

# 4 ELEVATION - 4

3/8" = 1'-0"


(C) 2023 by KEILEY & KASSA COMMUNITIES LLC.  
All rights, specifications and other documents prepared by the designer  
and consultants for this project are instruments of Kassabit LLC for use  
with respect to this project and unless otherwise provided, Kassabit  
will be deemed the author of these documents and shall retain all  
copyright, law, statutory and other reserved rights, including the copyrights.  
Architectural drawings, specifications and other documents for  
construction and reference are prohibited unless expressly authorized by  
KLLC in writing

Y & KASSA COMMUNITIES LLC - SERIES 1

<b>NO.</b>	
<b>E</b>	08/01/2024
<b>WN BY</b>	Author
<b>CHECKED BY</b>	Checker
<b>SE</b>	
<b>T NAME</b>	
<b>LDING ELEVATIONS</b>	

**UNIT NUMBER  
107**

CONTRACTOR  
KASSABILT LLC

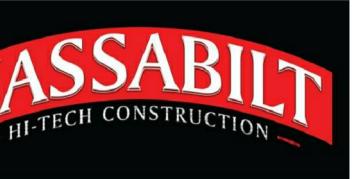

ISSUES

NO.	DATE	DESCRIPTION

**LOT 6, BLOCK 31/1615 MOUNT AUBURN**


500/502 S GLASGOW DR. DALLAS, TX 75223

PARCEL ID: 00000166051000000

DALLAS COUNTY, TEXAS



1 3D View 1

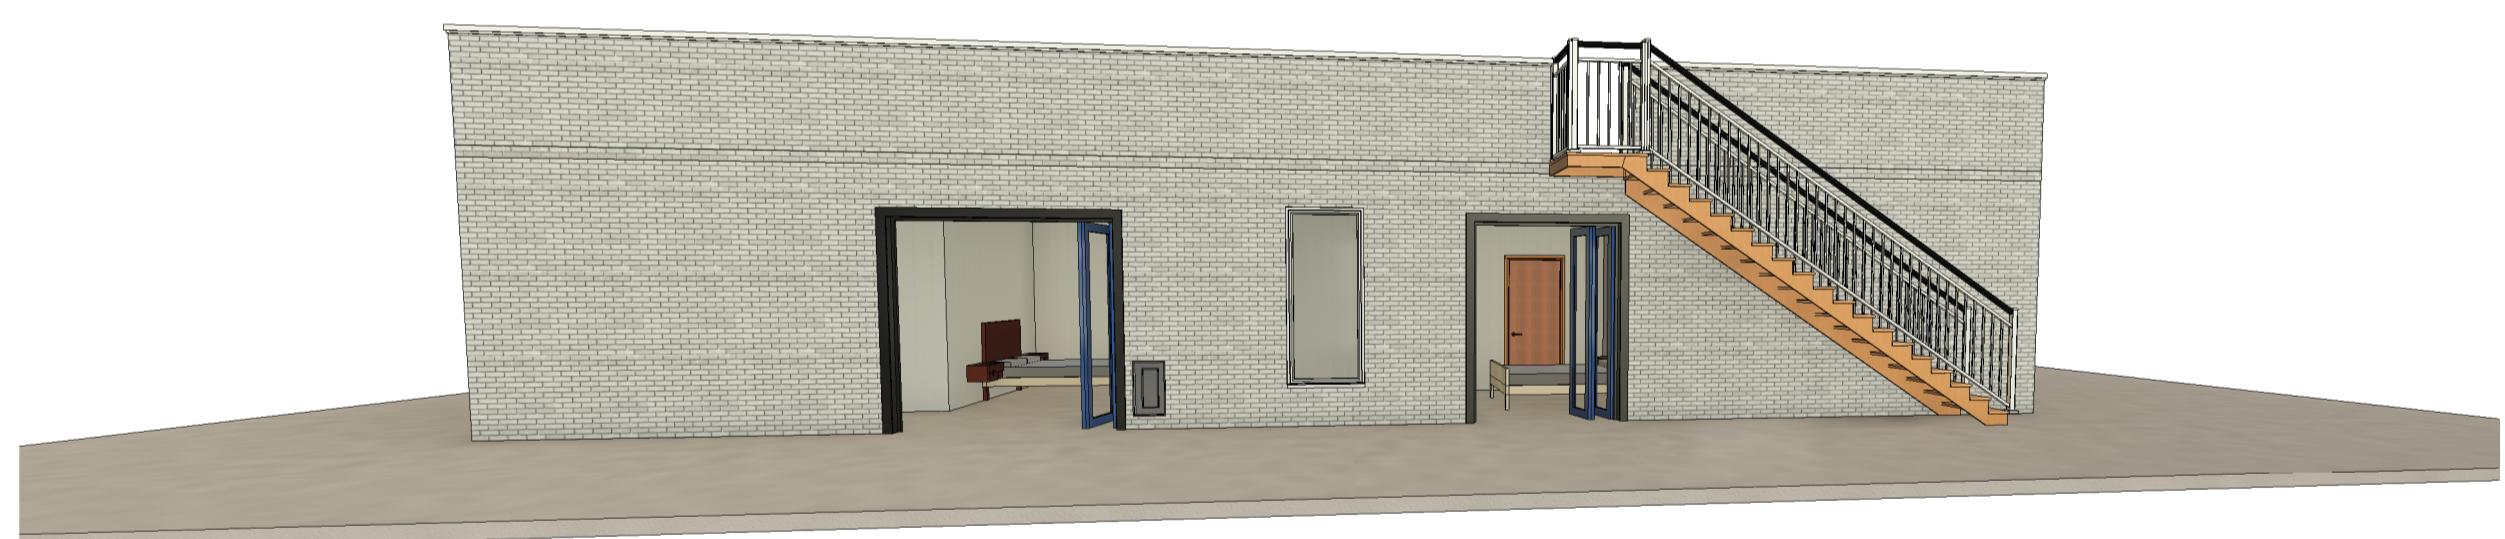

2 3D View 2



3 3D View 3



4 3D View 4

Copyright (C) 2023 by KELLEY & KASSA COMMUNITIES LLC.  
All drawings, specifications and other documents prepared by the designer  
are the sole property of Kassabilt LLC and may not be reproduced or disclosed to others  
solely with respect to this project and unless otherwise provided, Kassabilt  
LLC reserves all rights, including all rights under copyright law, statutory  
and common law, statutory and other reserved rights, including the copyrights.  
Copies of architectural drawings, specifications and other documents  
by unauthorized persons are prohibited unless expressly authorized by  
Kassabilt LLC in writing.

OWNER  
KELLEY & KASSA COMMUNITIES LLC - SERIES 1  
500/502 S GLASGOW DR.DALLAS, TX 75223

JOB NO.  
DATE 08/01/2024  
DRAWN BY Author  
CHECKED BY Checker  
PHASE  
SHEET NAME  
3D VIEWS

SHEET NUMBER  
**A115**